


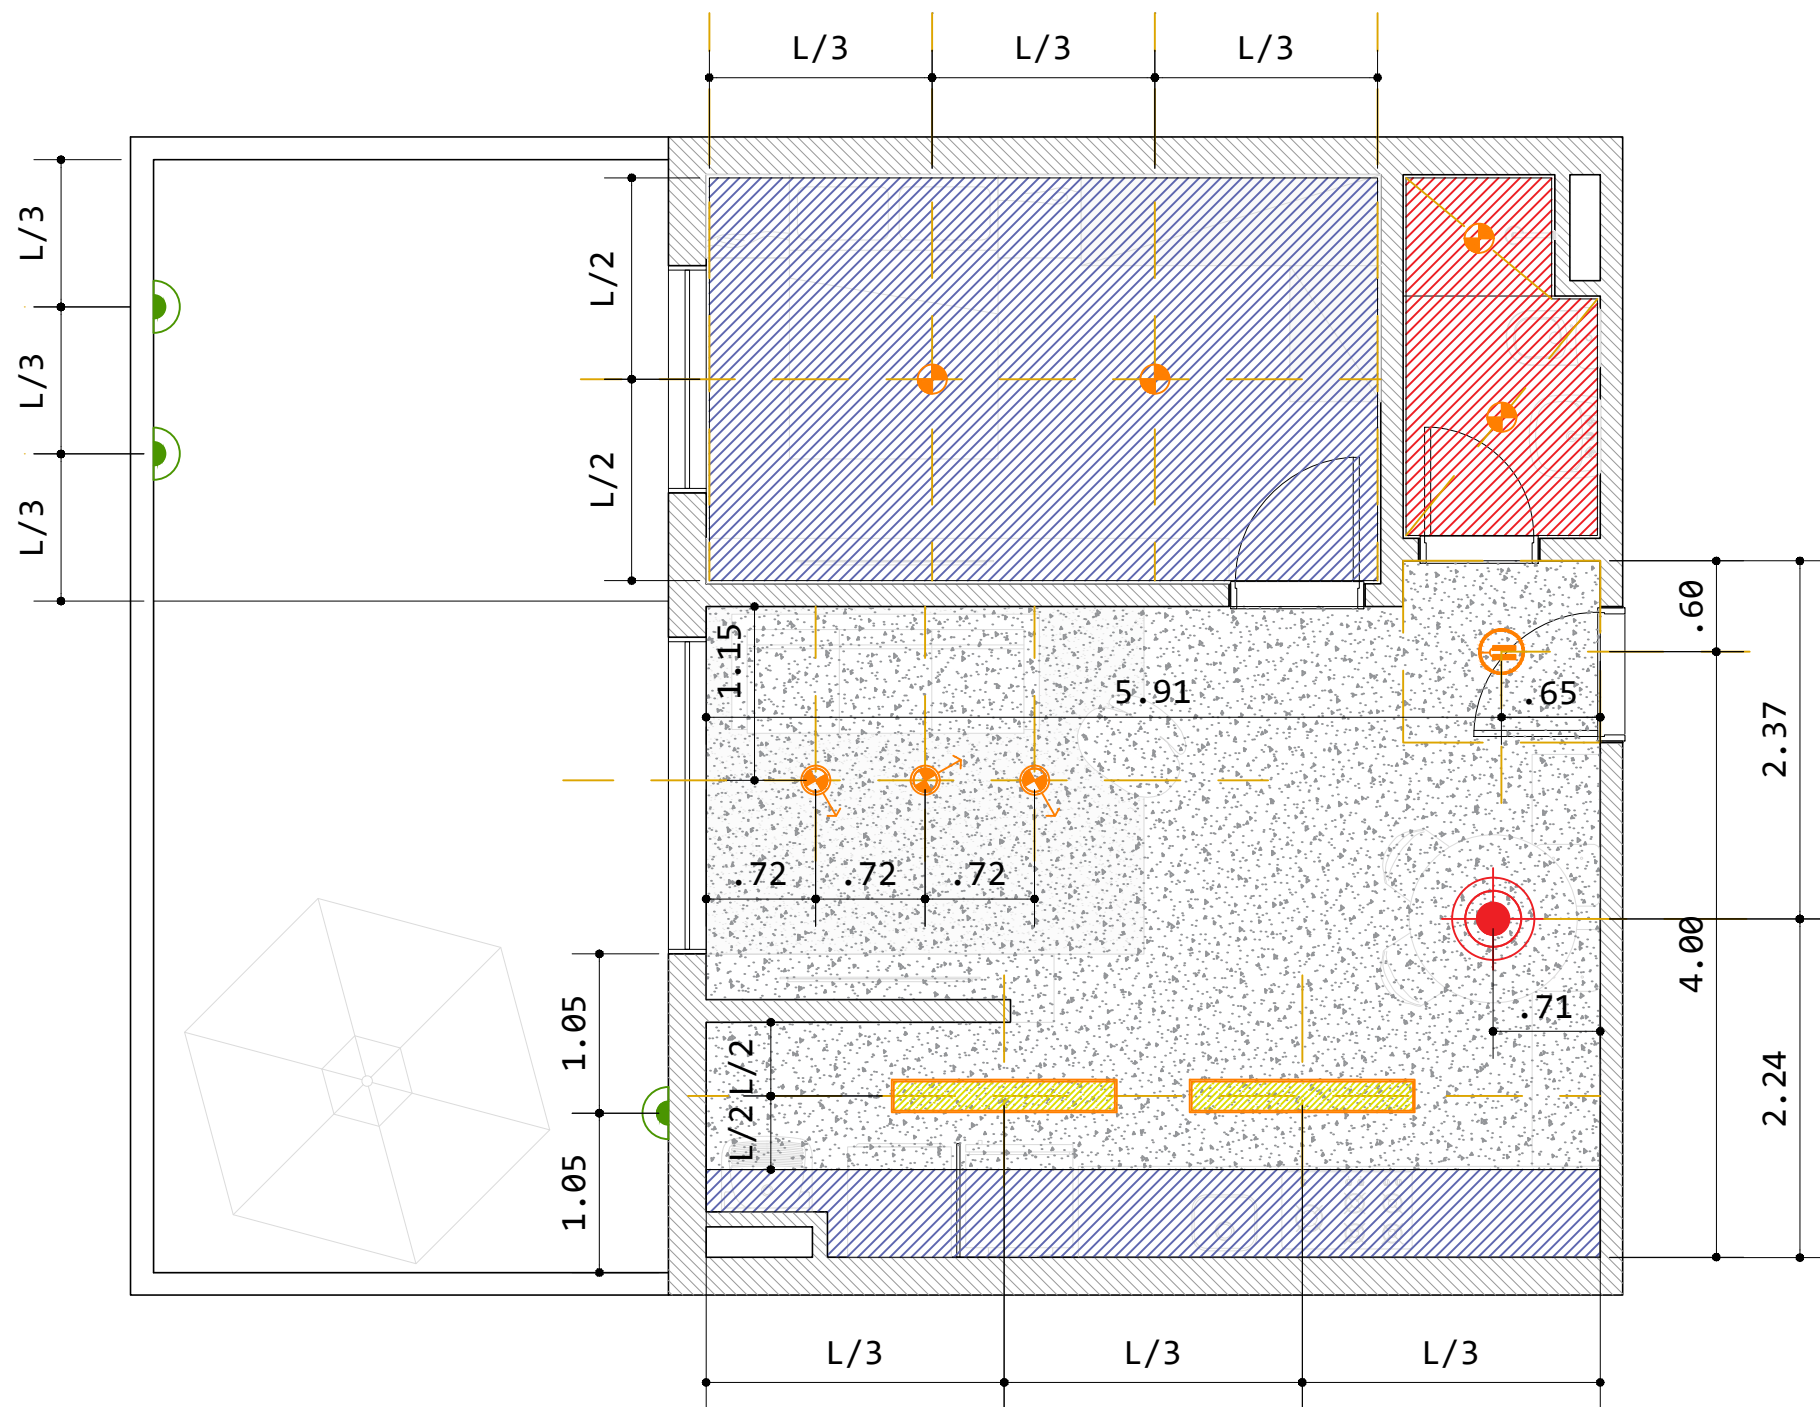

LEGENDA DE LUMINÁRIAS			
SÍMBOLO	LÂMPADA	TIPO	COR
	DICROICA	EMBUTIR	BRANCO
	LED BULBO	SOBREPOR	PRETO
	PAR20	PENDENTE DECORATIVO	DOURADO
	SPOT LED	TRILHO SOBREPOR	BRANCO
	PAR20	ARANDELA	BRANCO
	LED TUBULAR	EMBUTIR	BRANCO

LEGENDA DE FORRO			
SÍMBOLO	TIPO	P.D	OBS.
	FORRO DE GESSO	2,45	TABICA METÁLICA
	FORRO DE GESSO	2,30	TABICA METÁLICA
	LAJE APARENTE	2,65	SEM TABICA